

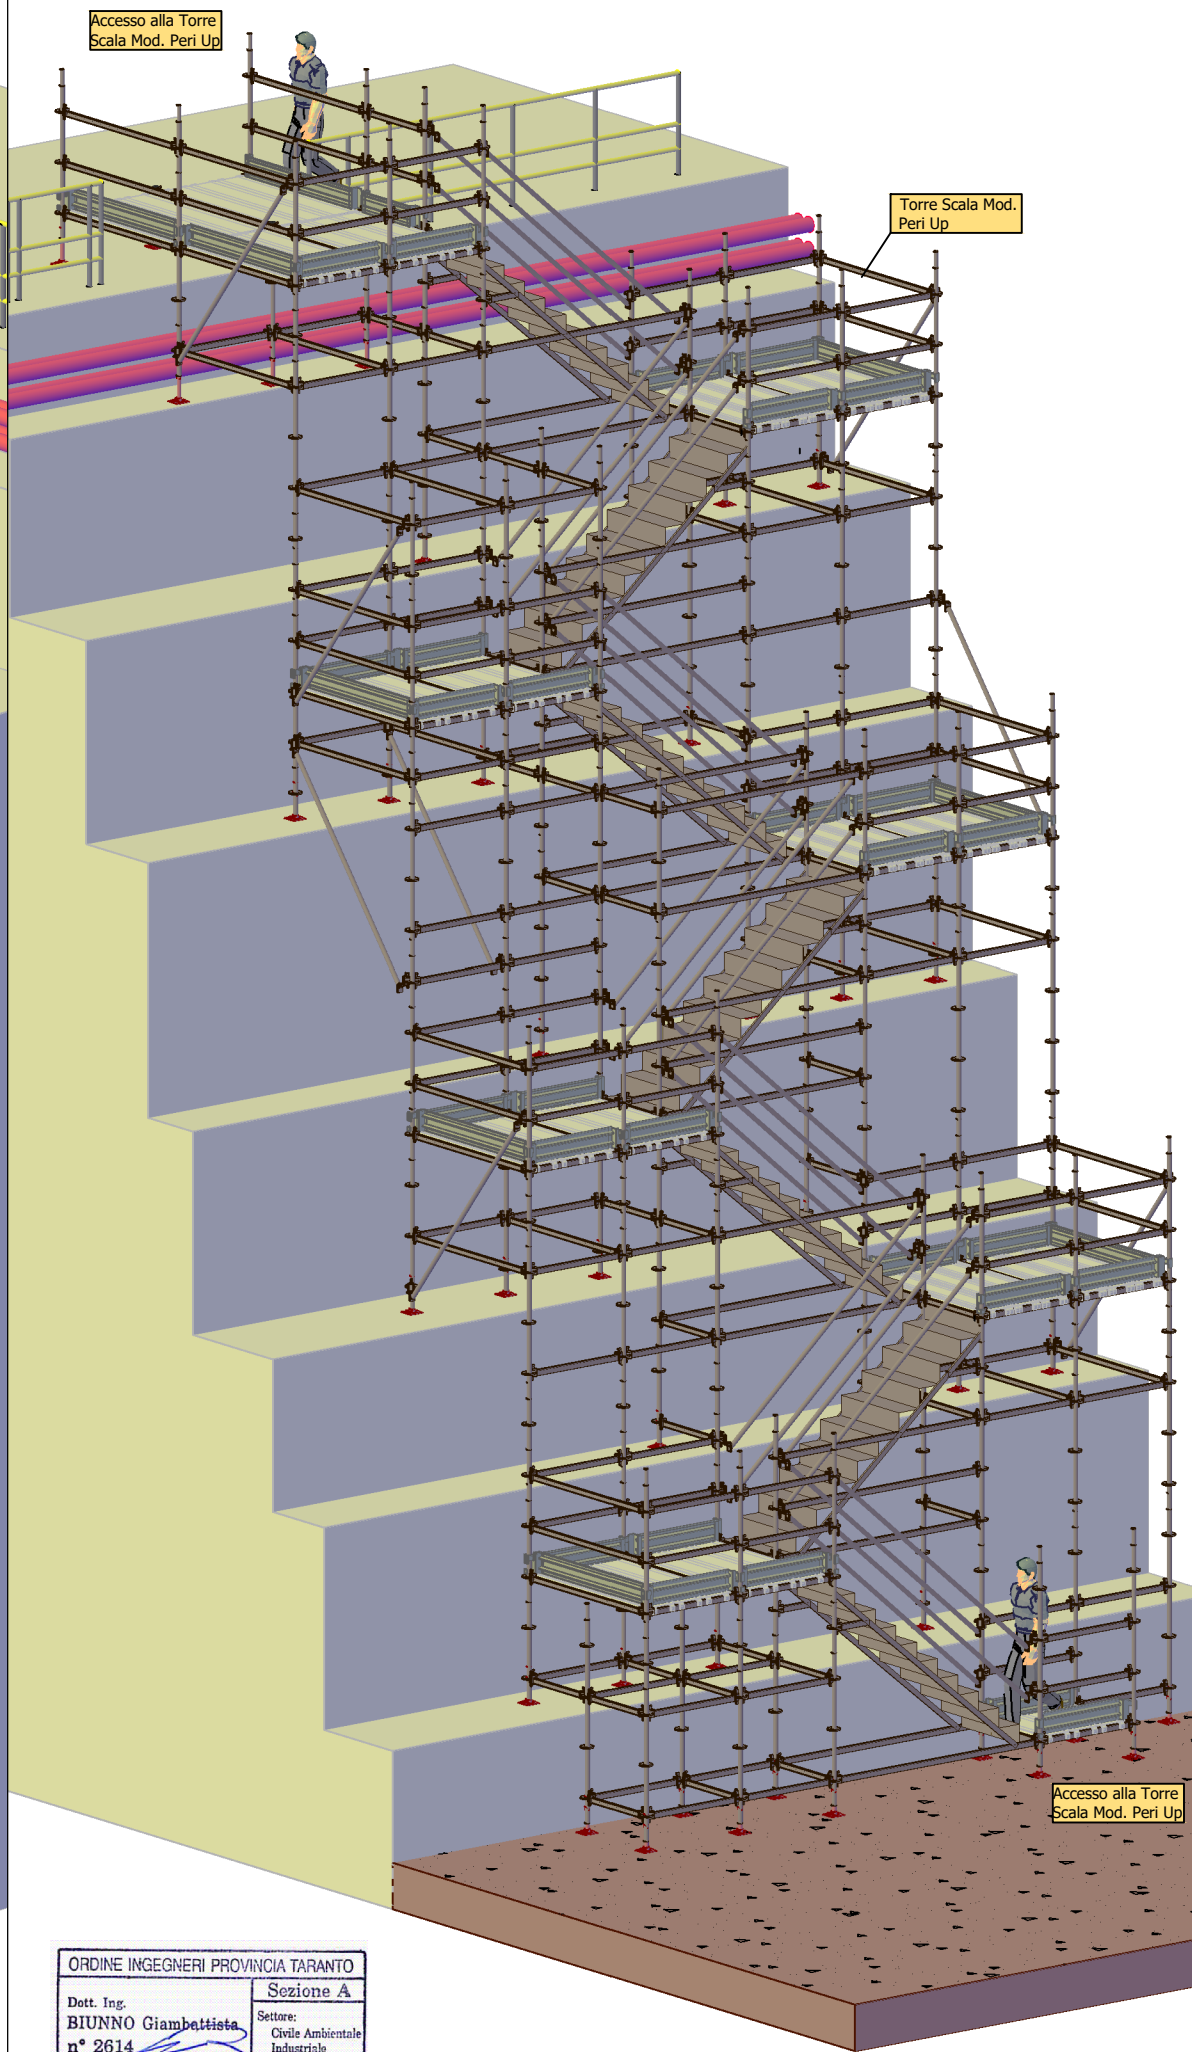


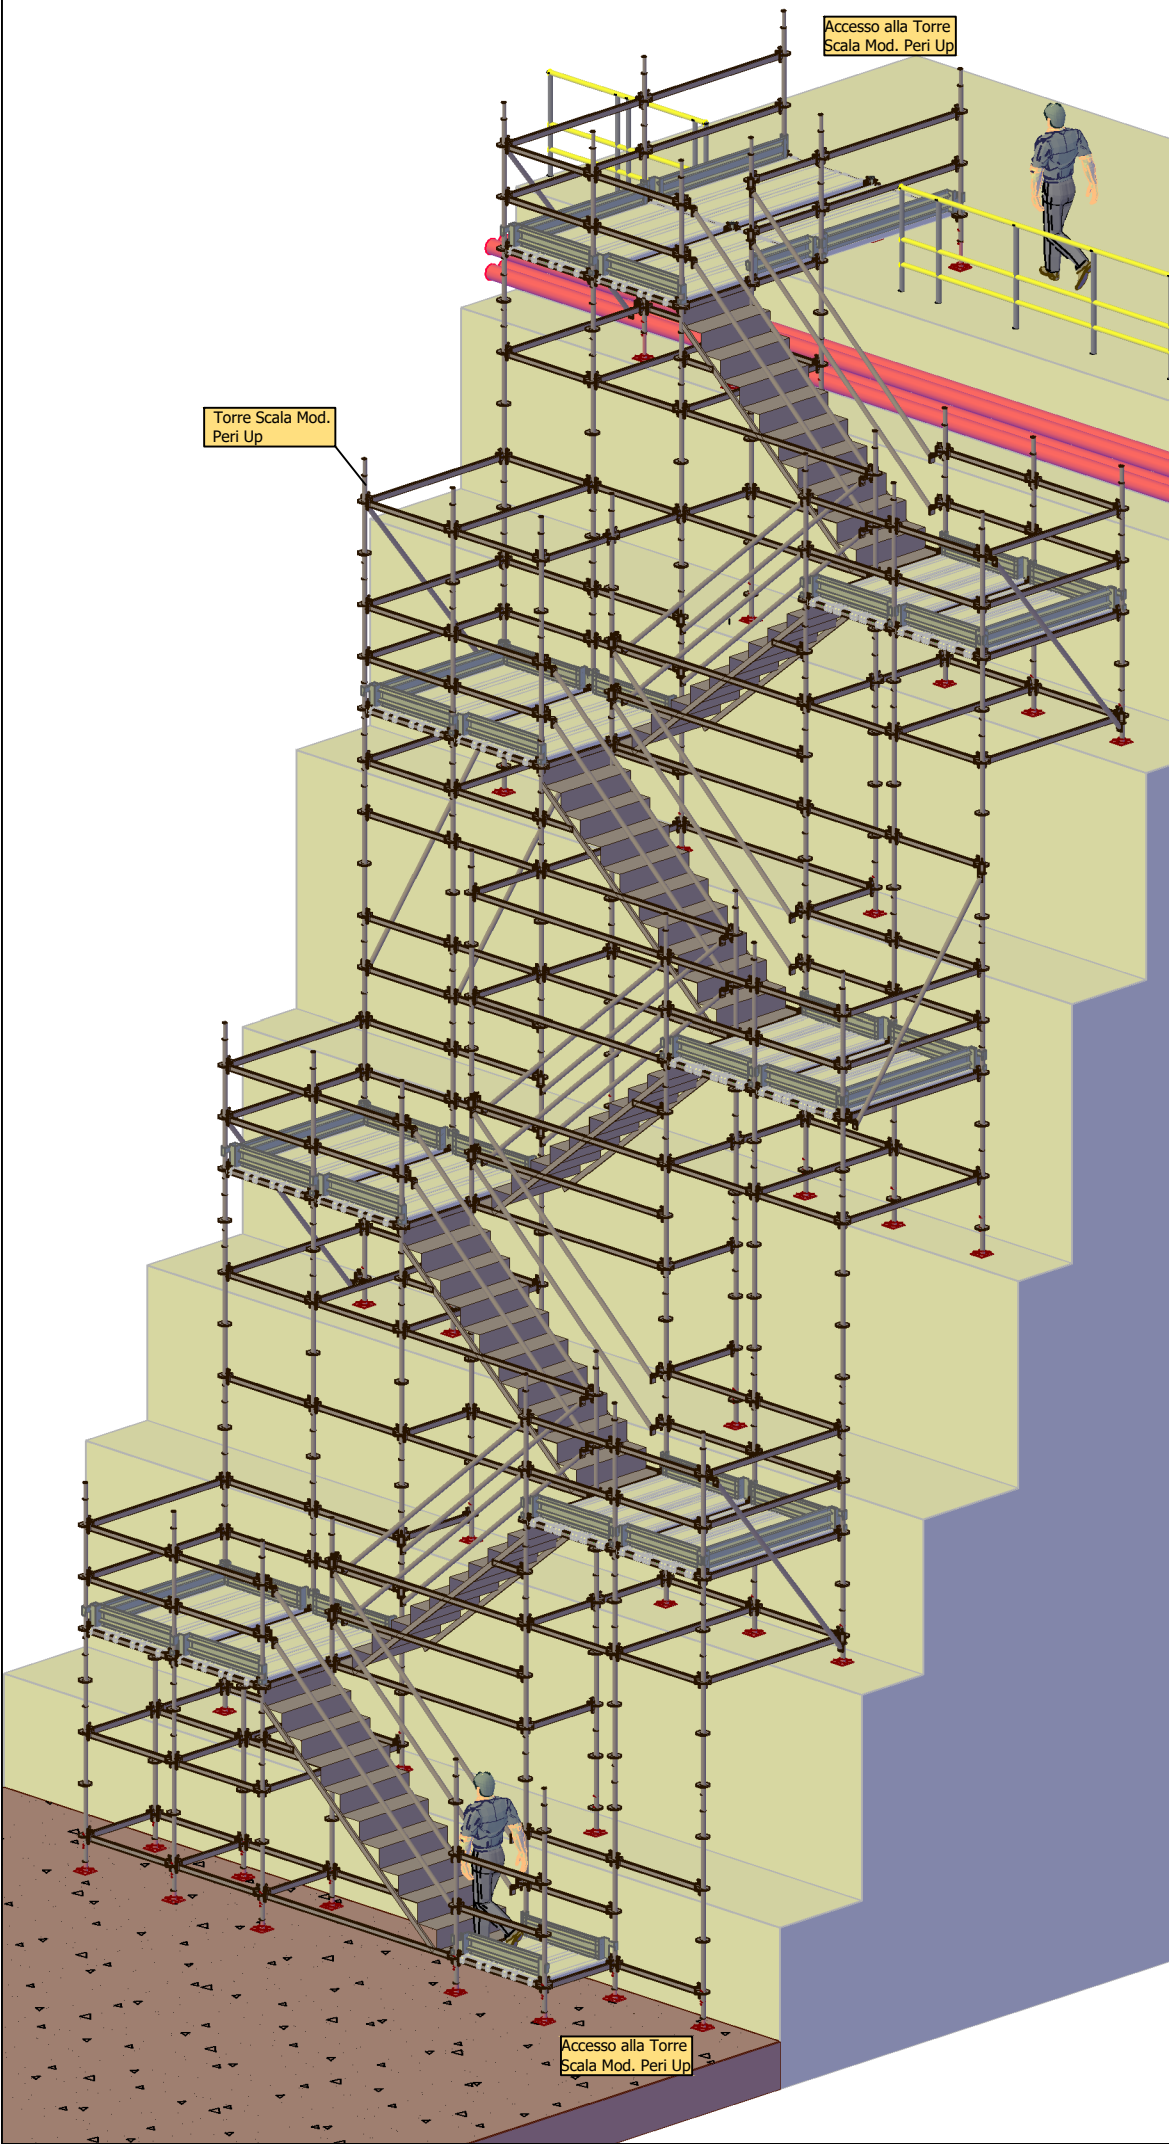

ORDINE INGEGNERI PROVINCIA TARANTO
Dott. Ing. BIUNNO Giambattista n° 2614
Sezione A
Settore: Civile Ambientale Industriale Infermazione

Stralcio Planimetria area di cantiere : Taranto - Arsenale M.M.

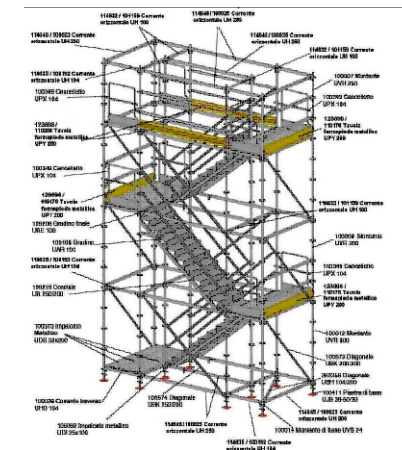

Legenda

- Elemento prefabbricato Mod. Scala a Torre PERI
- Elemento a tubo e giunti
- Botola metallica con scaletta
- Carico Massimo di Esercizio pari a 150 kg/m²
- Piani di lavoro in elementi metallici orizzontali
- = Ancoraggio a Tassello di tipo meccanico

COMUNE DI TARANTO ARSENALE MILITARE MARITTIMO DI TARANTO

Attività di accesso all'interno del Bacino Ferrati per attività di verifica delle zone lesionate - Comune di Taranto

Tavola n°1 - Vista Assonometrica

COMMESSA: Numero Commessa: n° /2025 Numero Pi.M.U.S. : 135_2025	UBICAZIONE CANTIERE: COMUNE DI TARANTO ARSENALE MILITARE MARITTIMO
IMPRESA ESECUTRICE MONT.- SMONT. PONTEGGIO: 	COMMITTENTE: ARSENALE MILITARE MARITTIMO
DATA: 07 - 01 - 2026	EMISSIONE: Revisione 02
DISEGNATO : Geom. Nunzio GIANNATTASIO	CONTROLLATO : Dott. Ing. Giambattista BIUNNO
VISTO: Sig. Giuseppe LIGORIO	