




Figura 1 in rosso recinzione, in verde accesso mezzi di lavoro (camion, gru, PLE), in blu accesso pedonale. In giallo parcheggio auto

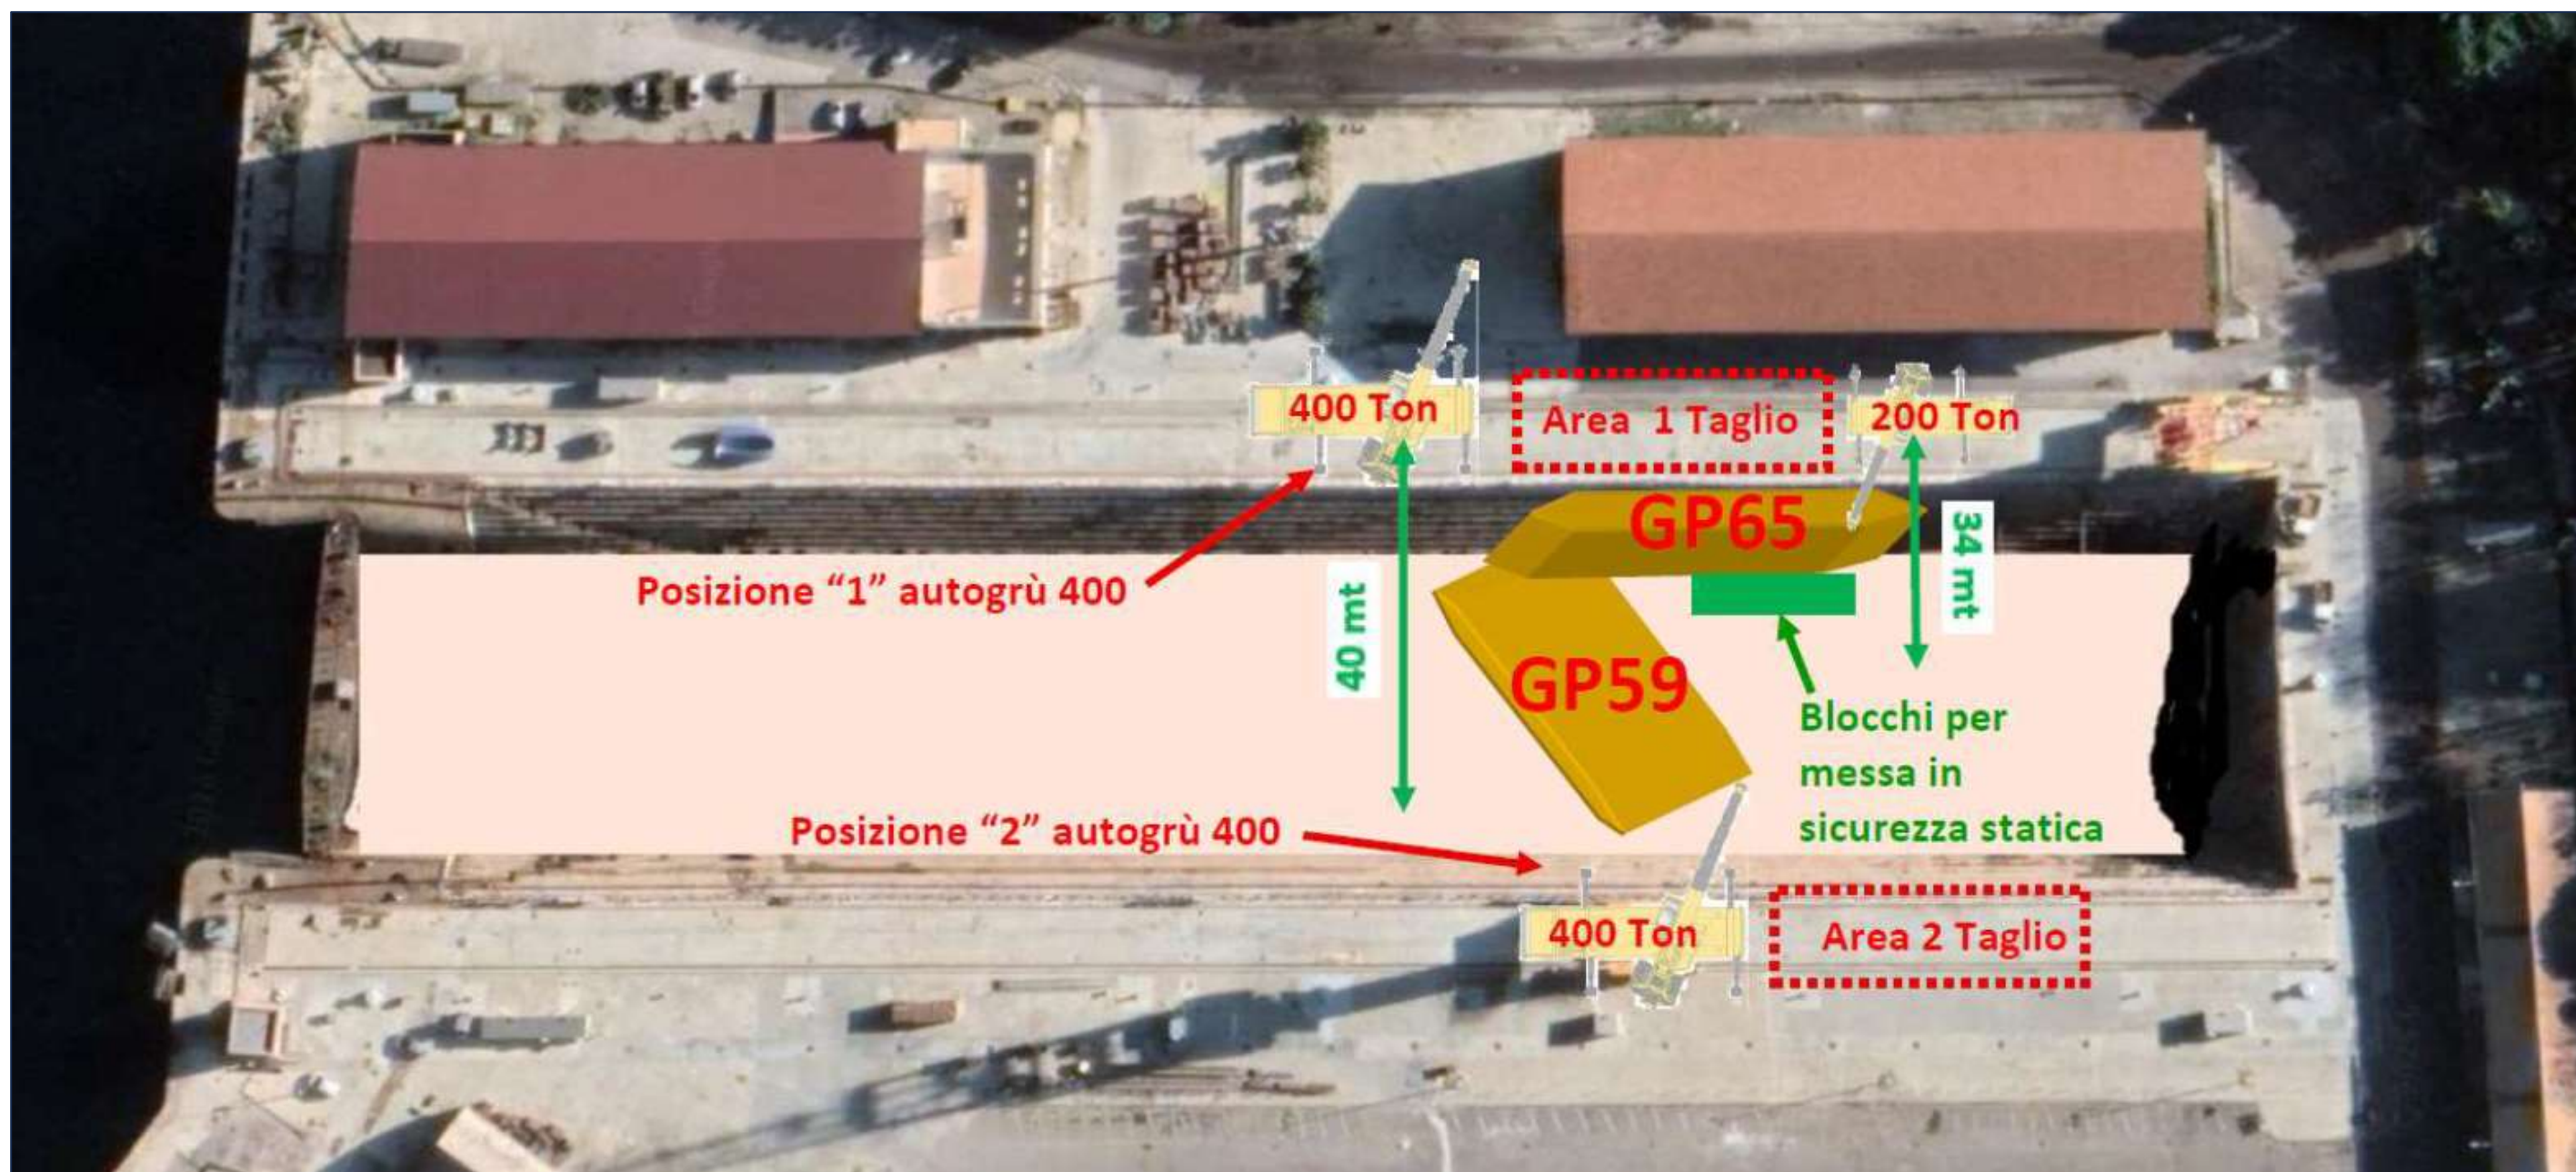

Dallo schema sopra rappresentato vengono indicate: l'area di riduzione volumetrica tratteggiata in rosso (dove la pavimentazione sarà protetta da lamieroni). Sono indicati i posizionamenti delle due tipologie di autogrù. In particolare la 400 Ton in una prima fase (posizione "1") svolgerà i sollevamenti delle sezioni di grandezza maggiore della barca porta "GP65", successivamente i sollevamenti delle sezioni rimanenti della stessa proseguiranno con l'autogrù 200 Ton. Nel frattempo l'autogrù 400 Ton si sposterà nel lato opposto del bacino (posizione "2") per effettuare i sollevamenti delle sezioni barca porta denominata "GP59".